

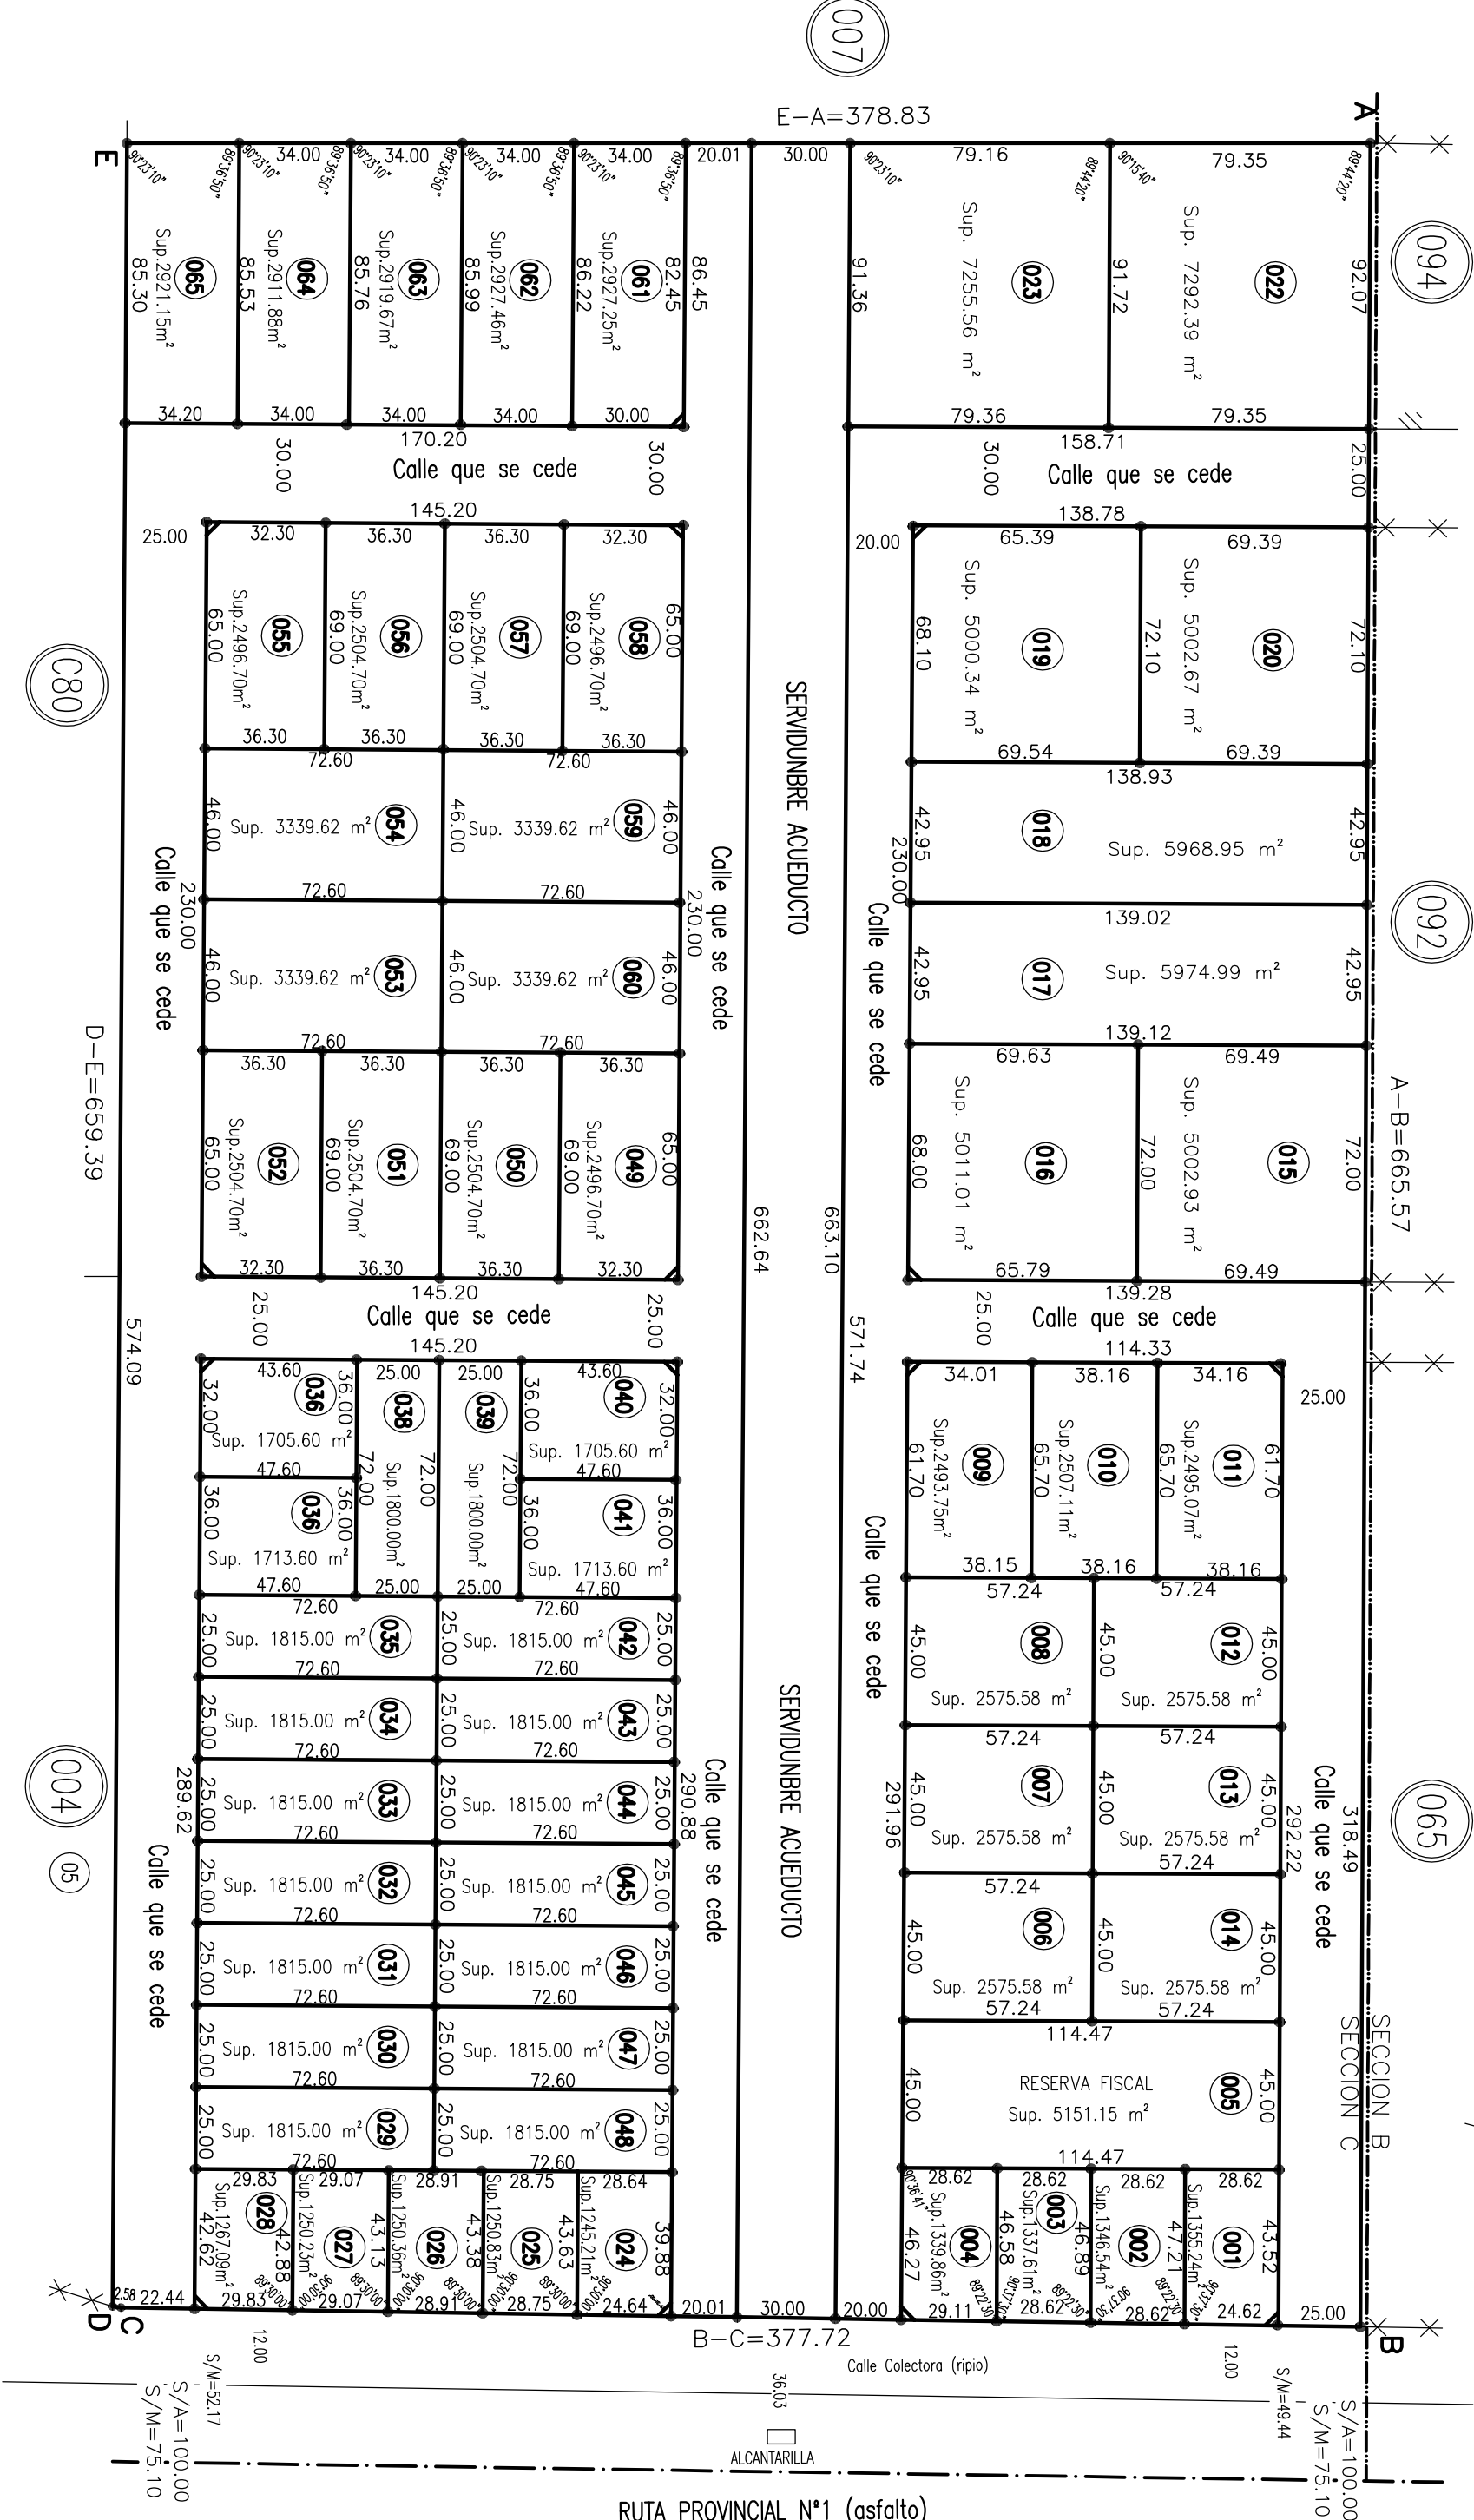
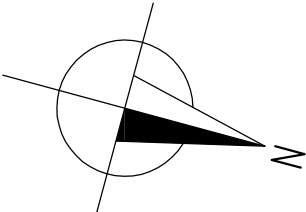


PROYECTO FAZ GEOMETRICA

ESCALA 1 : 2000

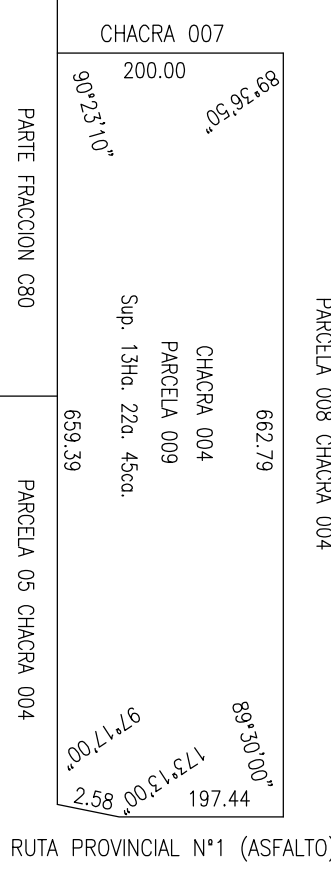

CROQUIS SEGUN PLANO 783-2021

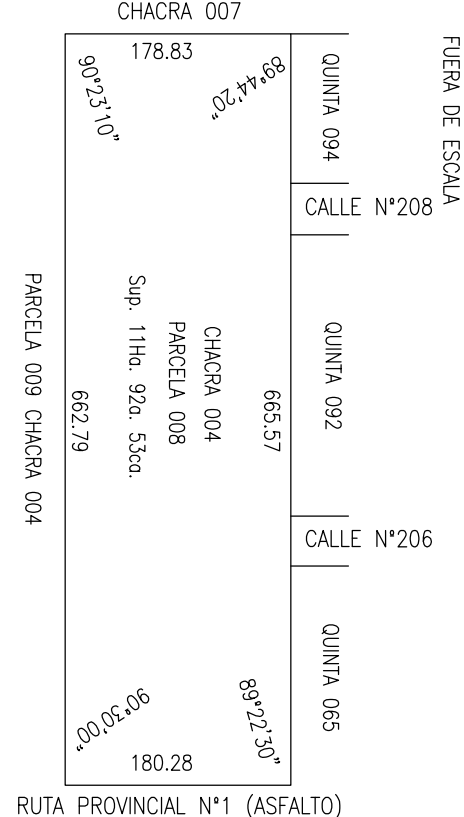

BALANCE DE SUPERFICIES

|                                              |              |
|----------------------------------------------|--------------|
| SUPERFICIE POR SUMA DE PARCELAS S./MENSURA   | 184047.05 m² |
| SUPERFICIE CALLE QUE SE CEDE S./MENSURA      | 62179.88 m²  |
| SUPERFICIE OCHAVAS QUE SE CEDEN S./MENSURA   | 120.09 m²    |
| SUPERFICIE RESERVA FISCAL QUE SE CEDE        | 5151.15 m²   |
| SUPERFICIE TOTAL SEGUN MENSURA               | 251498.17 m² |
| SUPERFICIE POR SUMA DE PARCELAS SEGUN TITULO | 251498.00 m² |
| DIFFERENCIA EN MAS                           | 0.17 m²      |

PROVINCIA DE RIO NEGRO

DEPARTAMENTO : ADOLFO ALSINA

VIEDMA

MENSURA PARTICULAR CON UNIFICACION Y FRACCIONAMIENTO

PARCELAS 03 y 04 CHACRA 004

PROPIETARIO:

ENREPAVI

INSCRIPCION DE DOMINIO

PARCELA

MATRICULA

03

18-9014

04

18-9015

ANTECEDENTES:

TITULOS DE PROPIEDAD

PLANOS DE MENSURA: 104-1975, 106-1975, 783-2021, 132-82;

NOTAS:

FECHA DEL INFORME DE DOMINIO: - 2023

SE COLOCARON MOJONES DE HIERRO SEGUN RES. 047/05

LOS ANGULOS NO INDICADOS SON DE 90° a 270°

DOMICILIO DEL PROPIETARIO: PARQUE INDUSTRIAL 8500- VIEDMA

SERVICIOS PUEBLOS: ENERGIA ELECTRICA; AGUA

LOS ANCHOS DE CALLES ESTAN DIBUADOS FUERA DE ESCALA

CANTIDAD DE PARCELAS: SESENTA Y CUATRO (64)

FECHA DE MENSURA: DICIEMBRE 2023

JORGE DANIEL MERRINO

AGRI-MENSOR

INSCR. D.G.C.VI.de R.N. N°607

INSCR. LEY 5216 - MATRICULA: (CPA) 3453

Dem.: M. Aguir N°269 2do piso-Viedma-TE:15615261

NOMENCLATURA CATASTRAL

DEPARTAMENTO CATASTRAL

18

CIRCUNSCRIPCION

1

SECCION

C

MANZANAS

VER PLANO

PARCELAS

VER PLANO

| NOMENCLATURA CATASTRAL DE ORIGEN |   |   |     |         |
|----------------------------------|---|---|-----|---------|
| DC                               | C | S | CH  | PARCELA |
| 18                               | 1 | C | 004 | 03      |
| 18                               | 1 | C | 004 | 04      |