

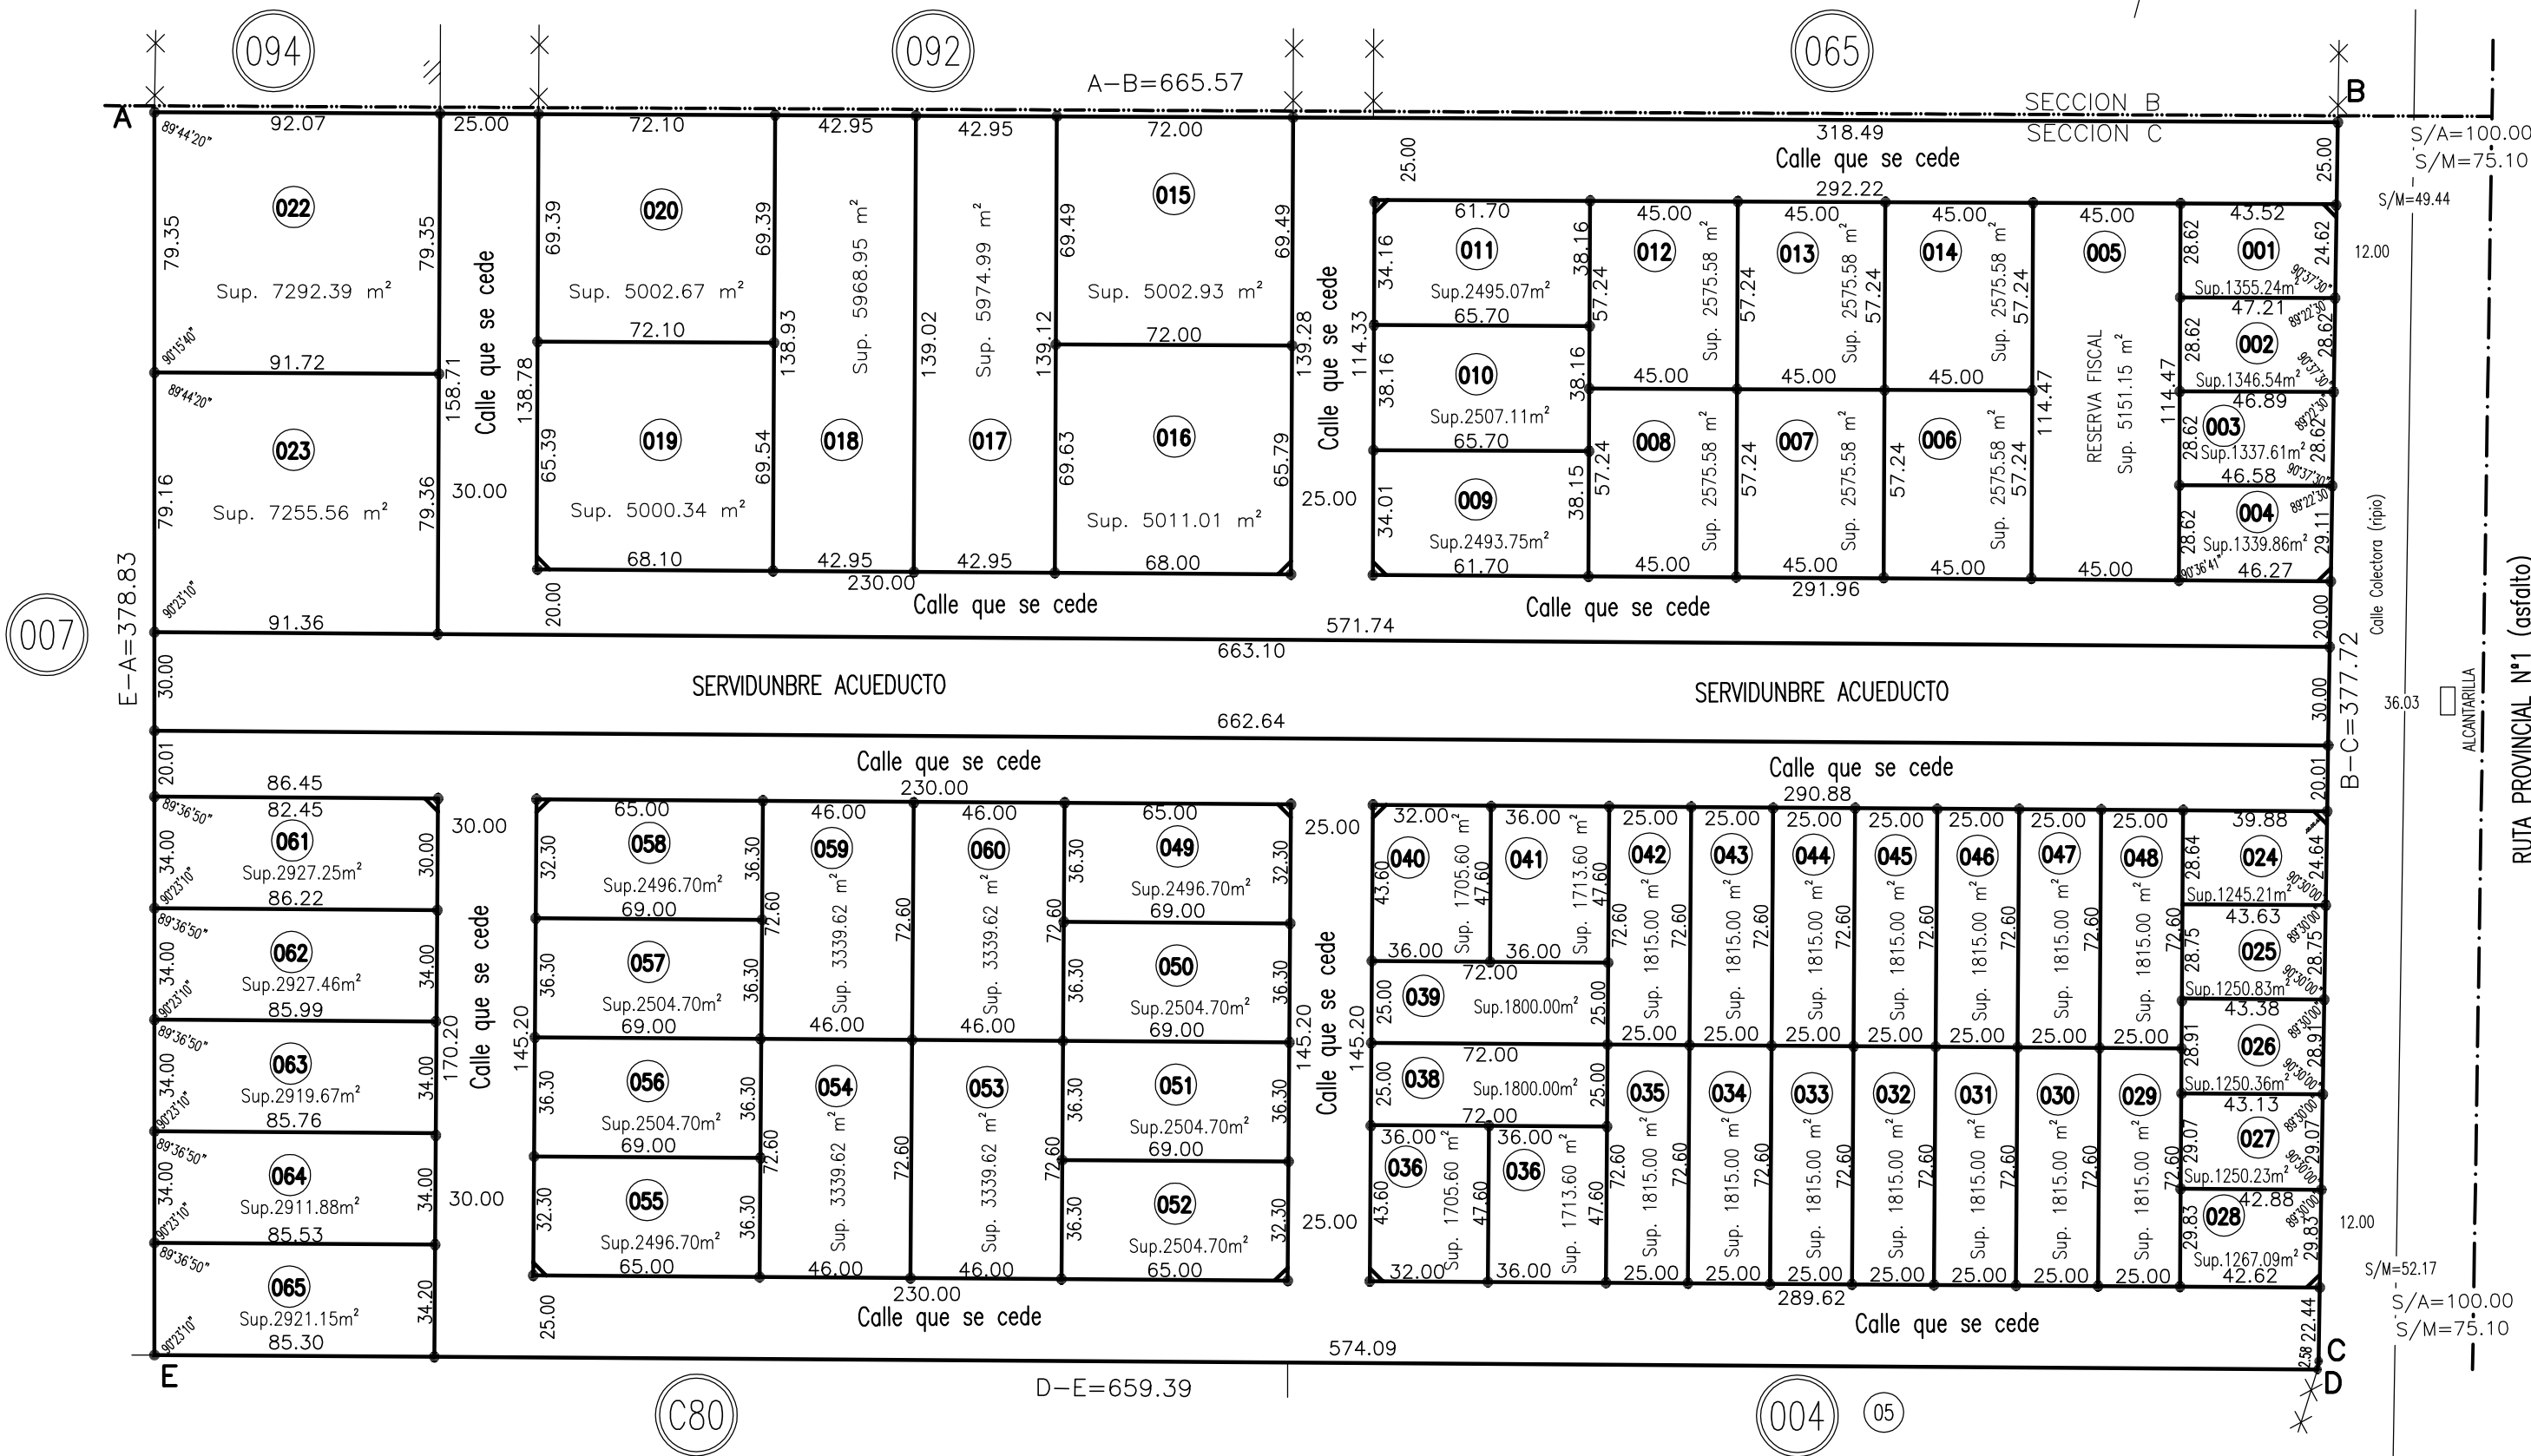


PROYECTO FAZ GEOMETRICA

ESCALA 1 : 2000

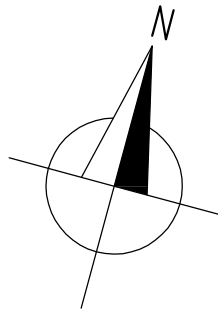

CROQUIS SEGUN PLANO 783-2021

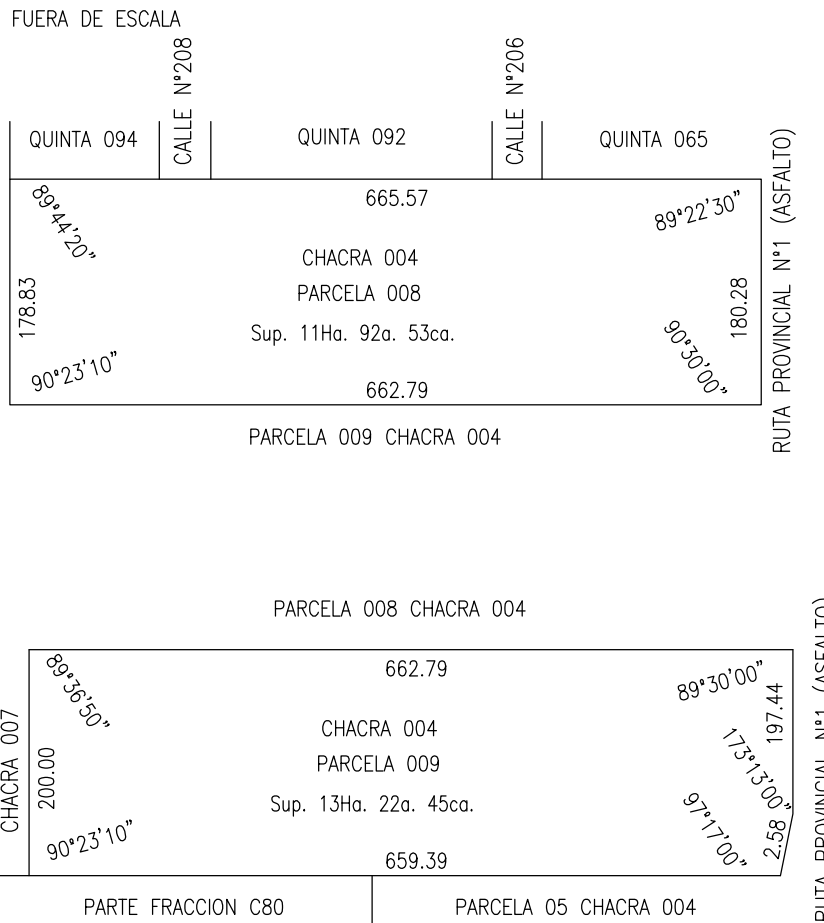

BALANCE DE SUPERFICIES

SUPERFICIE POR SUMA DE PARCELAS S/MENSURA	184047.05 m ²
SUPERFICIE CALLE QUE SE CEDE S/MENSURA	62179.88 m ²
SUPERFICIE OCHAVAS QUE SE CEDEN S/MENSURA	120.09 m ²
SUPERFICIE RESERVA FISCAL QUE SE CEDE	5151.15 m ²
SUPERFICIE TOTAL SEGUN MENSURA	251498.17 m ²
SUPERFICIE POR SUMA DE PARCELAS SEGUN TITULO	251498.00 m ²
DIFERENCIA EN MAS	0.17 m ²

PROVINCIA DE RIO NEGRO

DEPARTAMENTO : ADOLFO ALSINA

-2024

NOMENCLATURA CATASTRAL DE ORIGEN				
DC	C	S	CH	PARCELA
18	1	C	004	03
18	1	C	004	04

VIEDMA

MENSURA PARTICULAR CON UNIFICACION Y FRACCIONAMIENTO
PARCELAS 03 y 04 CHACRA 004

PROPIETARIO:

ENREPAVI

INSCRIPCION DE DOMINIO

OBSERVACIONES:

PARCELA	MATRICULA
03	18-9014
04	18-9015

ANTECEDENTES: TITULOS DE PROPIEDAD
PLANOS DE MENSURA: 104-1975; 106-1975; 783-2021; 132-82;

NOTAS: FECHA DEL INFORME DE DOMINIO: - -2023
SE COLOCARON MOJONES DE HIERRO SEGUN RES. 047/05
LOS ANGULOS NO INDICADOS SON DE 90° ò 270°
DOMICILIO DEL PROPIETARIO: PARQUE INDUSTRIAL 8500- VIEDMA
SERVICIOS PUBLICOS: ENERGIA ELECTRICA; AGUA
LOS ANCHOS DE CALLES ESTAN DIBUJADOS FUERA DE ESCALA

CANTIDAD DE PARCELAS: SESENTA Y CUATRO (64)

FECHA DE MENSURA: DICIEMBRE 2023

JORGE DANIEL MEIRIÑO

AGRIMENSOR
INSCR. D.G.C.yT.de R.N. N°607
INSCR. LEY 5216 - MATRICULA: (CPA) 3453
Dom.: M. Aguiar N°269 2do piso-Viedma-TE:15615261

NOMENCLATURA CATASTRAL

DEPARTAMENTO	CATASTRAL	18
CIRCUNSCRIPCION		1
SECCION		C
MANZANAS	VER PLANO	
PARCELAS	VER PLANO	